


RZUT PARTERU			A-01 nr. rysunku
326201_1.1029.7 identyfikator czynnika ewidencyjnego			1:100 skala
POLITECHNIKA MORSKA W SZCZECINIE, ul. Wały Chrobrego 1-2, 70-500 Szczecin komputer, adres projektant			PW stadium
mgr inż. arch. Magdalena Kuźeła nr upr. 8/W/MOKK/2009 upr. bud. w specj. arch. do proj. bez ogr.	sprawdzający: mgr inż. arch. Jacek Szlis nr upr. BI/96/01 upr. bud. w specj. arch. do proj. bez ogr.	asystent: mgr inż. arch. Aleksandra Podkościelna mgr inż. arch. Jakub Chyliński	ARCH. branża
			06/2024 data

 


ZNACZENIA	
ZNACZENIA PRZEGRÓD	
	ŚCIANY KONSTRUKCYJNE ŻELBETOWE PREFABRYKOWANE
	ŚCIANY DZIAŁOWE ŻELBETOWE PREFABRYKOWANE
	ŚCIANY DZIAŁOWE SILIKATOWE
	ELEMENTY ISTNIEJĄCE DO USUNIĘCIA
	FASADA SZKLANA SŁUPOWO-RYGLOWA
	ZNACZENIE POZIOMY WYSOKOŚCIOWEGO POWIERZCHNI WARSTWY WYKONCZENIOWEJ
	WEJŚCIE DO BUDYNKU
WE	WYJŚCIE EWAKUACYJNE
ELEWACJA PÓŁNOČNA	ZNACZENIE ELEWACJI
	
ROZWIĄZANIA PRZECIWPÓŻAROWE	
	ŚCIANA O ODPORNOŚCI OGNIOWEJ REI 120
	DRZWI W KLASIE ODPORNOŚCI OGNIOWEJ EI 30 DYMOSZCZELNE
	DRZWI W KLASIE ODPORNOŚCI OGNIOWEJ EI 60
	DRZWI W KLASIE ODPORNOŚCI OGNIOWEJ EI 60 DYMOSZCZELNE
	FASADA SZKLANA SŁUPOWO-RYGLOWA W KLASIE ODPORNOŚCI OGNIOWEJ EI 60
	HYDRANT WEWNĘTRZNY WNĘKOWY HP25
ZNACZENIA STOLARKI	
STOLARKA DRZWIOWA	
	<u>SZEROKOŚĆ PRZEJŚCIA W ŚWIEŁIE</u> <u>WYSOKOŚĆ PRZEJŚCIA W ŚWIEŁIE</u>
TYP STOLARKI DRZWIOWEJ	
FASADY SZKLANE	
	<u>SZEROKOŚĆ KONSTRUKCJI FASADY SZKLANEJ</u> <u>WYSOKOŚĆ KONSTRUKCJI FASADY SZKLANEJ</u>
TYP FASADY SZKLANEJ	
	

UWAGI OGÓLNE:

1. DOPUSZCZA SIĘ ZAMIANE MATERIAŁÓW LUB PRODUCENTÓW ZAPROPONOWANYCH W PROJEKcie, POZOSTAWIAJĄC TE SAME WŁAŚCIWOŚCI TECHNICZNE I ESTETYCZNE. W WYPADKACH ZMIAN MATERIAŁOWYCH NALEŻY UZYSKAĆ ZGODĘ INWESTORA, PROJEKTANTA I NAZDORCU AUTORSKIEGO, NA WSZELKIE ZMIANY MATERIAŁÓW ELEWACYJ BUDYNKU I PRZESZKLENIA NALEŻY UZYSKAĆ ZGODĘ MIEJSKIEGO KONSERWATORA ZABYTKÓW ORAZ PROJEKTANTA.
2. WSZYSTKIE ZAPROPONOWANE PRZEZ WYKONAWCĘ MATERIAŁY, URZĄDZENIA, ELEMENTY I TECHNOLOGIE, POWINNY SPEŁNIAĆ WSZYSTKIE ZAŁOŻONE W PROJEKcie PARAMETRY TECHNICZNE, ESTETYCZNE I FORMALNO-PRAWNE.
3. WSZYSTKIE MATERIAŁY, URZĄDZENIA I TECHNOLOGIE POWINNY POSIADAĆ PRZEWIDZIANE PRAWEM I ODPOWIEDNIMI PRZEPISAMI DOPUSZCZAJĄCE, ATESTY I CERTYFIKATY.
4. PRZED PRZYSTĘPIENIEM DO PRAC BUDOWLANYCH WSZYSTKIE WYMIARY NALEŻY SPRAWDZIĆ W NATURZE. W PRZYPADKU STwierDZENIA NIEZGODNOŚCI NALEŻY ZWRÓCIĆ SIĘ DO PROJEKTANTA.
5. PRZED PRZYSTĘPIENIEM DO PRAC BUDOWLANYCH WYMAGA SIĘ SPORZĄDZENIA PRZED WYKONANIEM PROJEKTU WARSZTATOWEGO FASAD SZKLANIACH, SZKŁANIEGO DACHU ŁĄCZNIKA I ELEMENTÓW PREFABRYKOWANYCH DO AKCEPTACJI PRZEZ PROJEKTANTA.

		ul. Wiertnicza 143A 02-952 Warszawa	
BUDOWA CENTRUM SYMULATORÓW PROMÓW I OFFSHORE WRAZ Z ŁĄCZNIKIEM DO BUDYNKU GŁÓWNEGO POLITECHNIKI MORSKIEJ W SZCZECINIE PRZY UL. WAŁY CHROBREGO 1-2, W RAMACH INWESTYCJI PN. "BUDOWA CENTRUM SYMULATORÓW PROMÓW I OFFSHORE ORAZ ROZBUDOWA, NADBUDOWA I PRZEBUDOWA ISTNIEJĄCEGO BUDYNKU SALI GIMNASTYCZNEJ NA AKADEMICKIE CENTRUM SYMULATORÓW WRAZ Z KOMPLEKSOWYM ZAGOSPODAROWANIEM DZIAŁKI OD STRONY UL. JAROWITA W SZCZECINIE"			
ul. Wały Chrobrego 1-2, 00-500 Szczecin			
razem, odnies			
RZUT POZIOMU +1		A-02 nr, rysunku	
326201_1.1029.7		1:100 skala	
identyfikator działki ewidencyjnej		PW studium	
POLITECHNIKA MORSKA W SZCZECINIE, ul. Wały Chrobrego 1-2, 70-500 Szczecin			
numer, adres projektant: mgr inż. arch. Magdalena Kuźela nr upr. 8/WMOKK/2009		sprawdzający: mgr inż. arch. Jacek Szlis nr upr. BI/96/01	
uwagi, bud. w specj. arch. do proj. bez ogr.		asystent: mgr inż. arch. Aleksandra Podkościelna mgr inż. arch. Jakub Chyliński	
		06/2024 data	

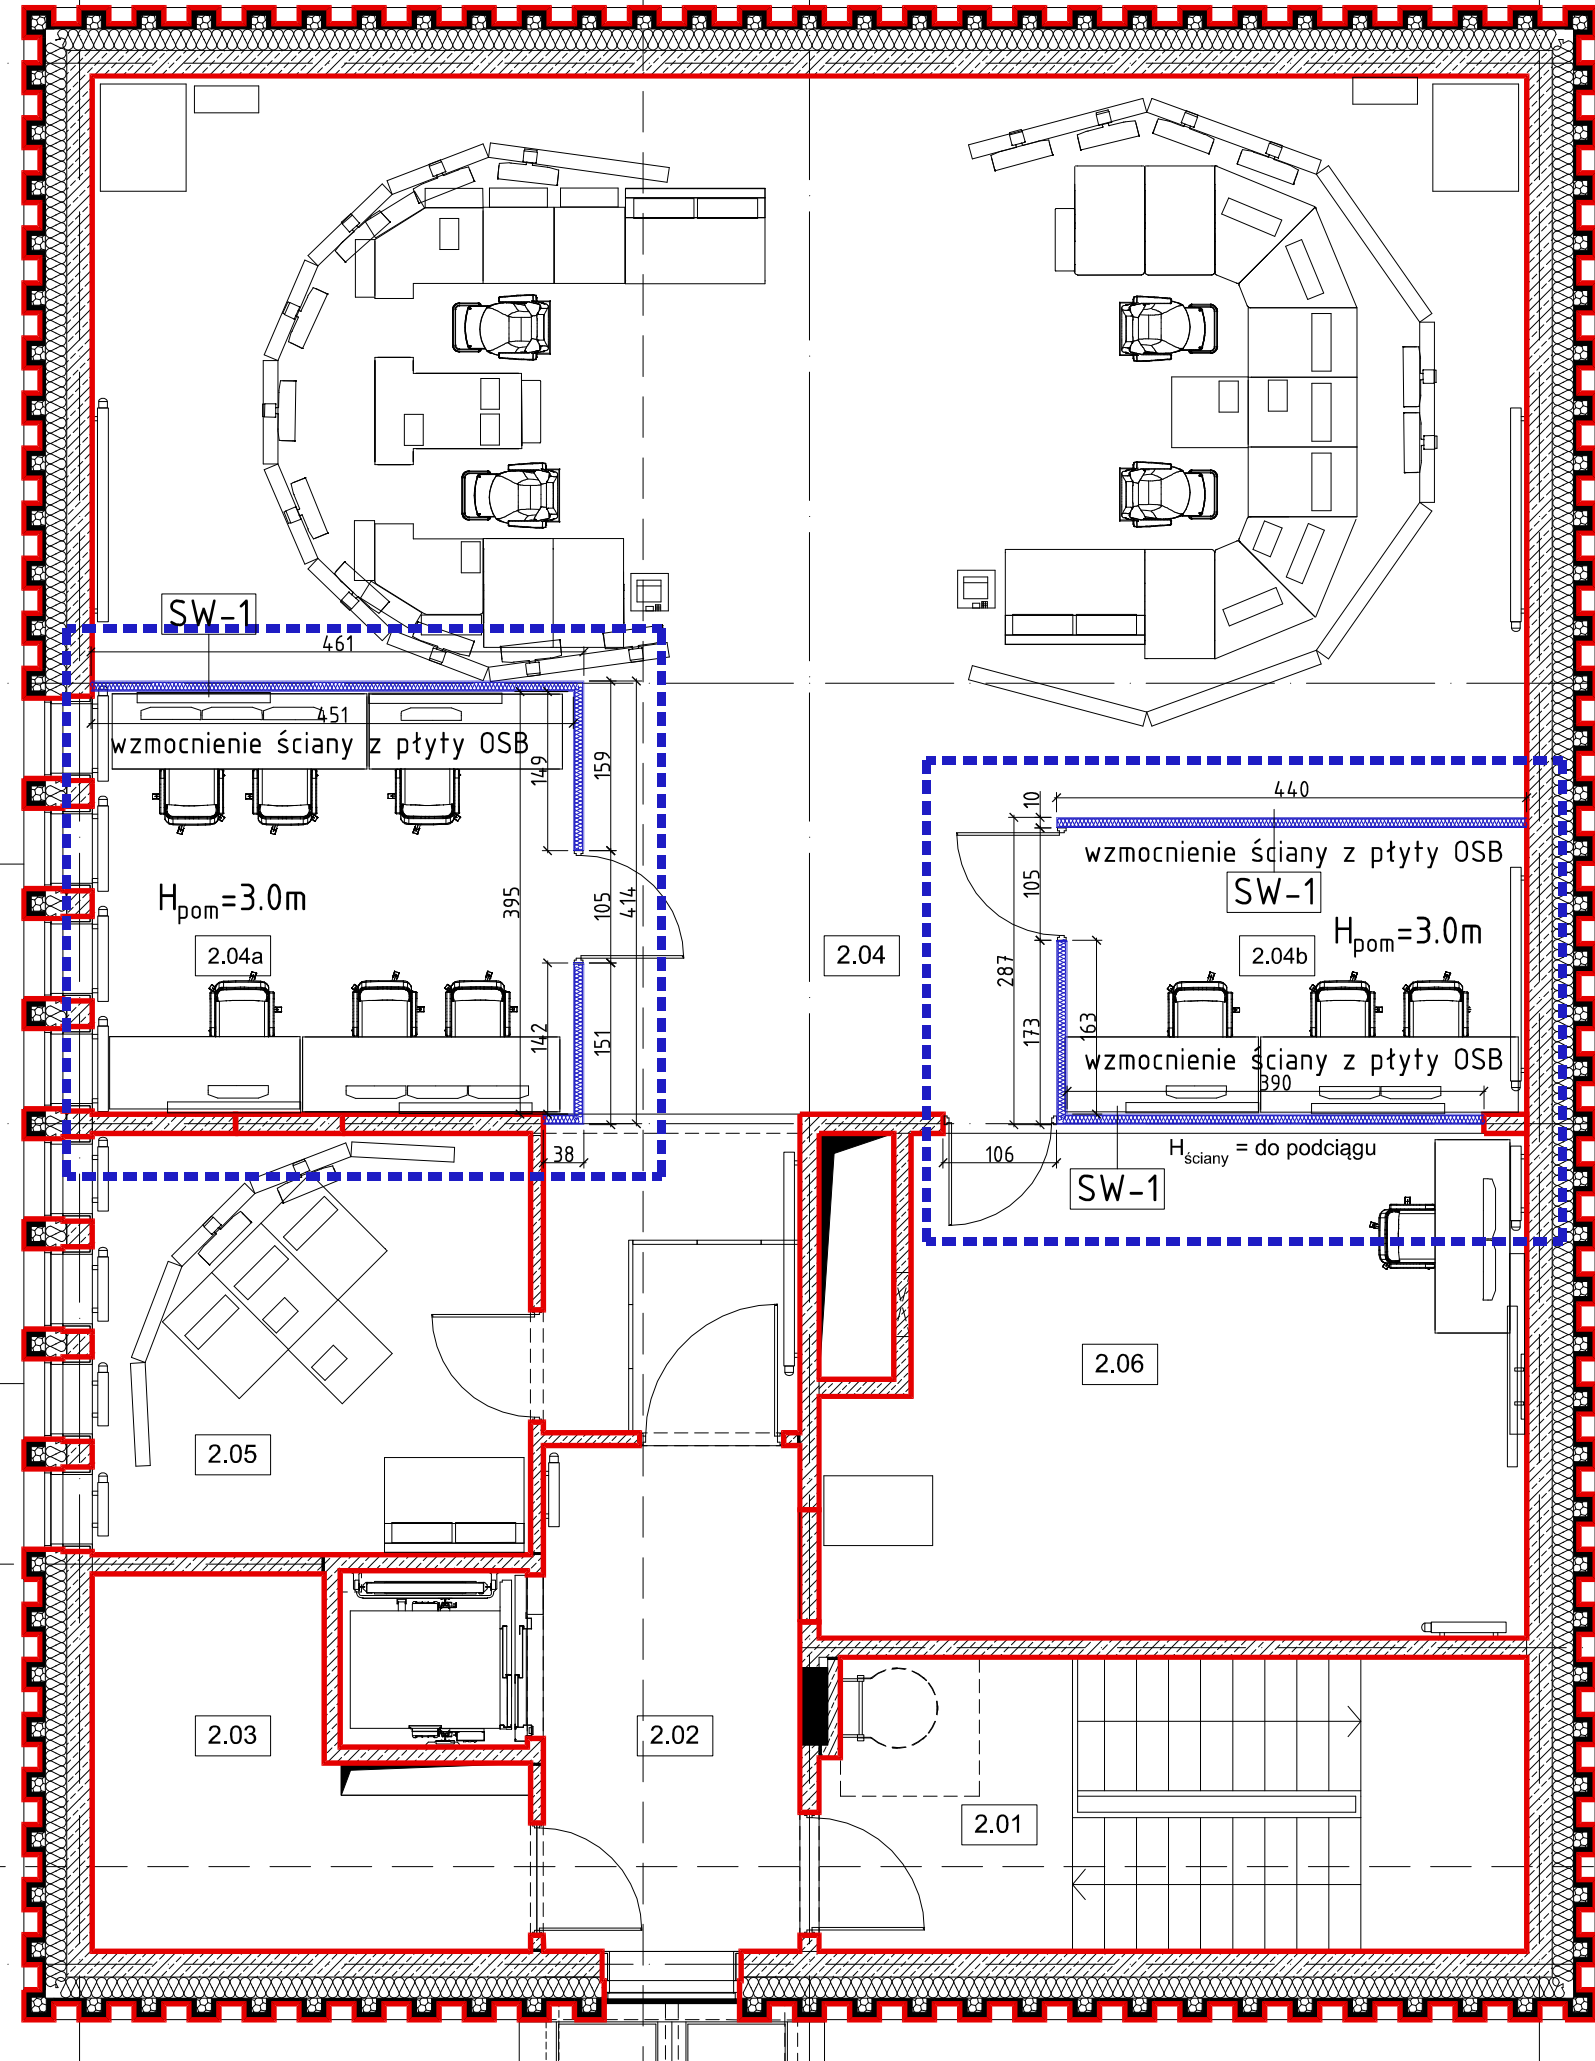

ZESTAWIENIE PRZEGRÓD		
ŚCIANY WEWNĘTRZNE		
SW-1	ŚCIANA DZIAŁOWA do pełnej wysokości	
	2,4cm	PODWÓJNA PŁYTA GK LUB RÓWNOWAŻNE
	7,5cm	WEŁNA SZKLANA NA PODKONSTRUKCJI Z PROFILI STAŁOWYCH CW75, NAROŻNIKI WZMOCNIONE PROFILAMI UA
	2,4cm	PODWÓJNA PŁYTA GK LUB RÓWNOWAŻNE

OZNACZENIA

OZNACZENIA PRZEGRÓD

- ZAKRES ROBÓT BUDOWLANYCH
- ŚCIANY KONSTRUKCYJNE ŻELBETOWE ISTNIEJĄCE
- ŚCIANY DZIAŁOWE PROJEKTOWANE

OPIS ROBÓT BUDOWLANYCH:

- WYKONANIE ŚCIANEK DZIAŁOWYCH W ZABUDOWIE SUCHEJ
- WYKONANIE SUFITU MODUŁOWEGO 60X60 (POMIESZCZENIA 2.04a I 2.04b).

UWAGA:

- WSZYSTKIE MATERIAŁY, URZĄDZENIA I TECHNOLOGIE POWINNY POSIADAĆ PRZEWIDZIANE PRAWEM I ODPOWIEDNIMI PRZEPISAMI DOPUSZCZENIA, ATESTY I CERTYFIKATY.
- PRZED PRZYSTĘPIENIEM DO PRAC BUDOWLANYCH WSZYSTKIE WYMIARY NALEŻY SPRAWDZIĆ W NATURZE. W PRZYPADKU STWIERDZENIA NIEZGODNOŚCI NALEŻY ZWRÓCIĆ SIĘ DO ZAMAWIAJĄCEGO.
- W RAMACH ROBÓT BUDOWLANYCH WYKONAWCA PRZENOSI NA SIEBIE GWARANCJE I RĘKOJMIE NA 60 MC W OBRĘBIE POMIESZCZENIA 2.04, 2.04a, 2.04b, 2.06.